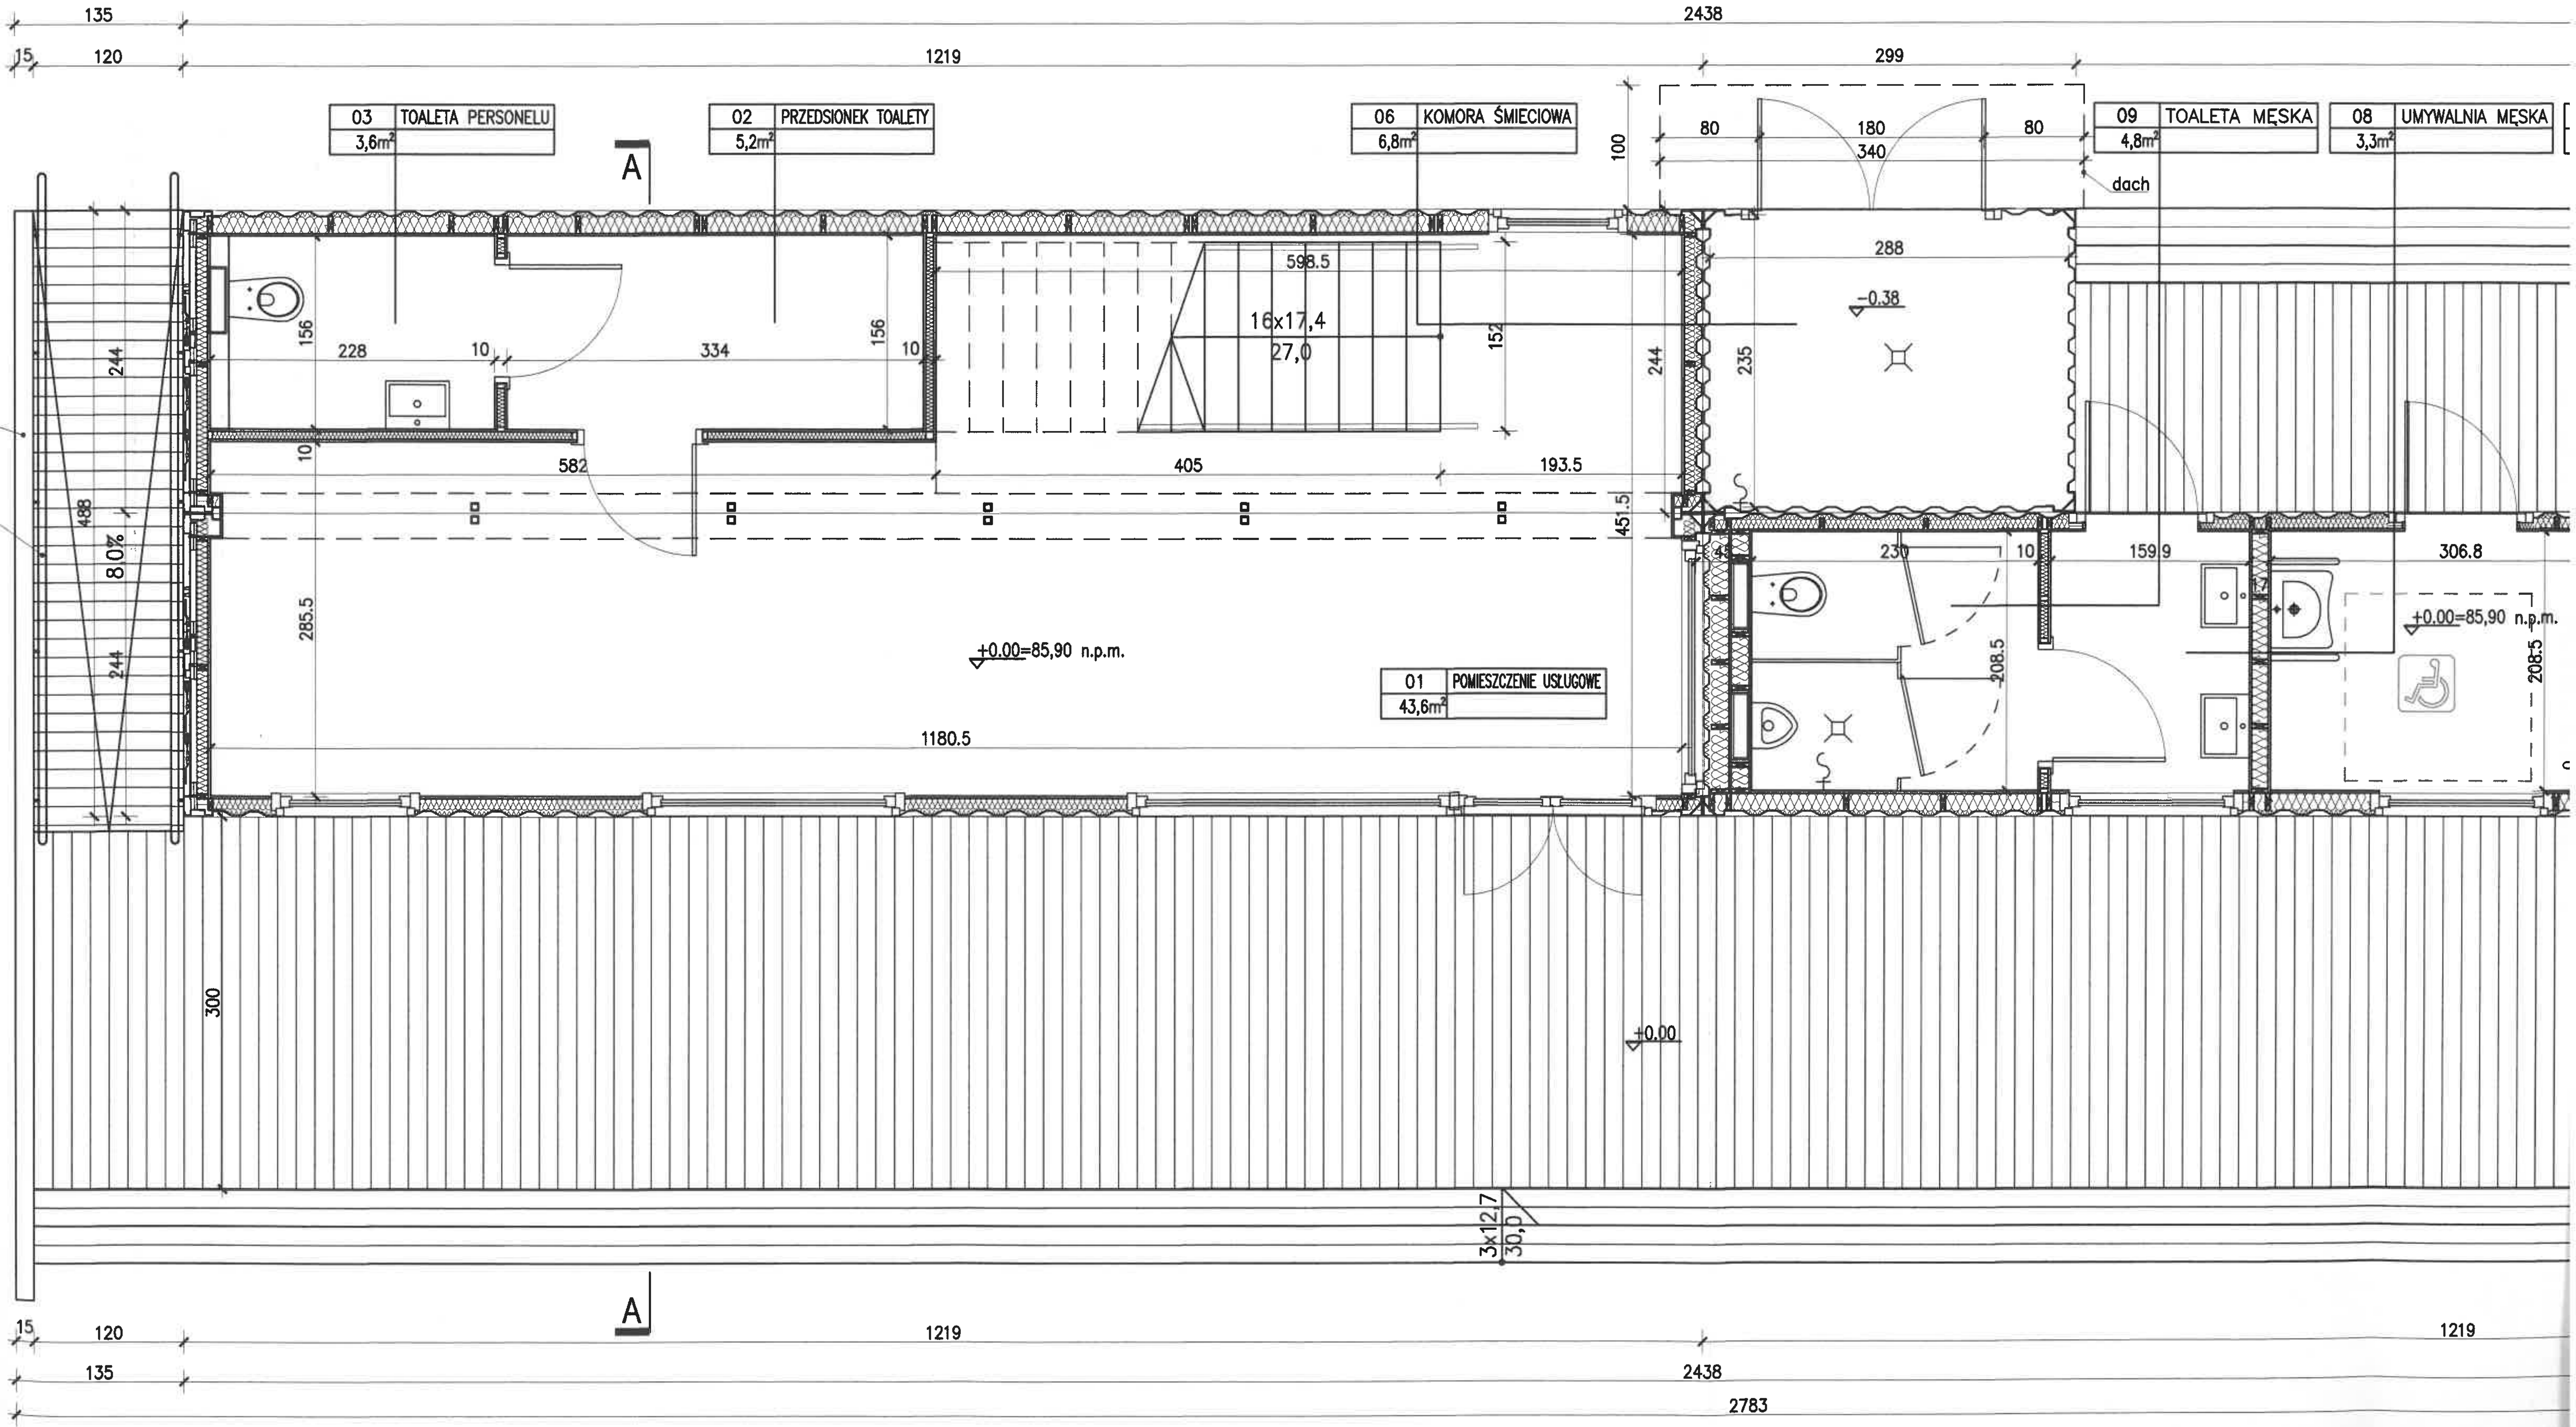
135
2438
15
120
1219
299
03 TOALETA PERSONELU
3,6m²
02 PRZEDSIONEK TOALETY
5,2m²
06 KOMORA ŚMIECIOWA
6,8m²
09 TOALETA MĘSKA
4,8m²
08 UMYWALNIA MĘSKA
3,3m²
A
100
80
180
340
80
dach
288
598.5
16x17,4
27,0
-0.38
156
228
10
334
156
10
152
244
235
244
488
8,0%
244
10
582
405
193.5
45.5
285.5
+0.00=85,90 n.p.m.
01 POMIESZCZENIE USŁUGOWE
43,6m²
1180.5
230
10
159.9
306.8
17
45
208.5
+0.00=85,90 n.p.m.
208.5
300
+0.00
3x12,7
30,0
A
15
120
1219
1219
135
2438
2783