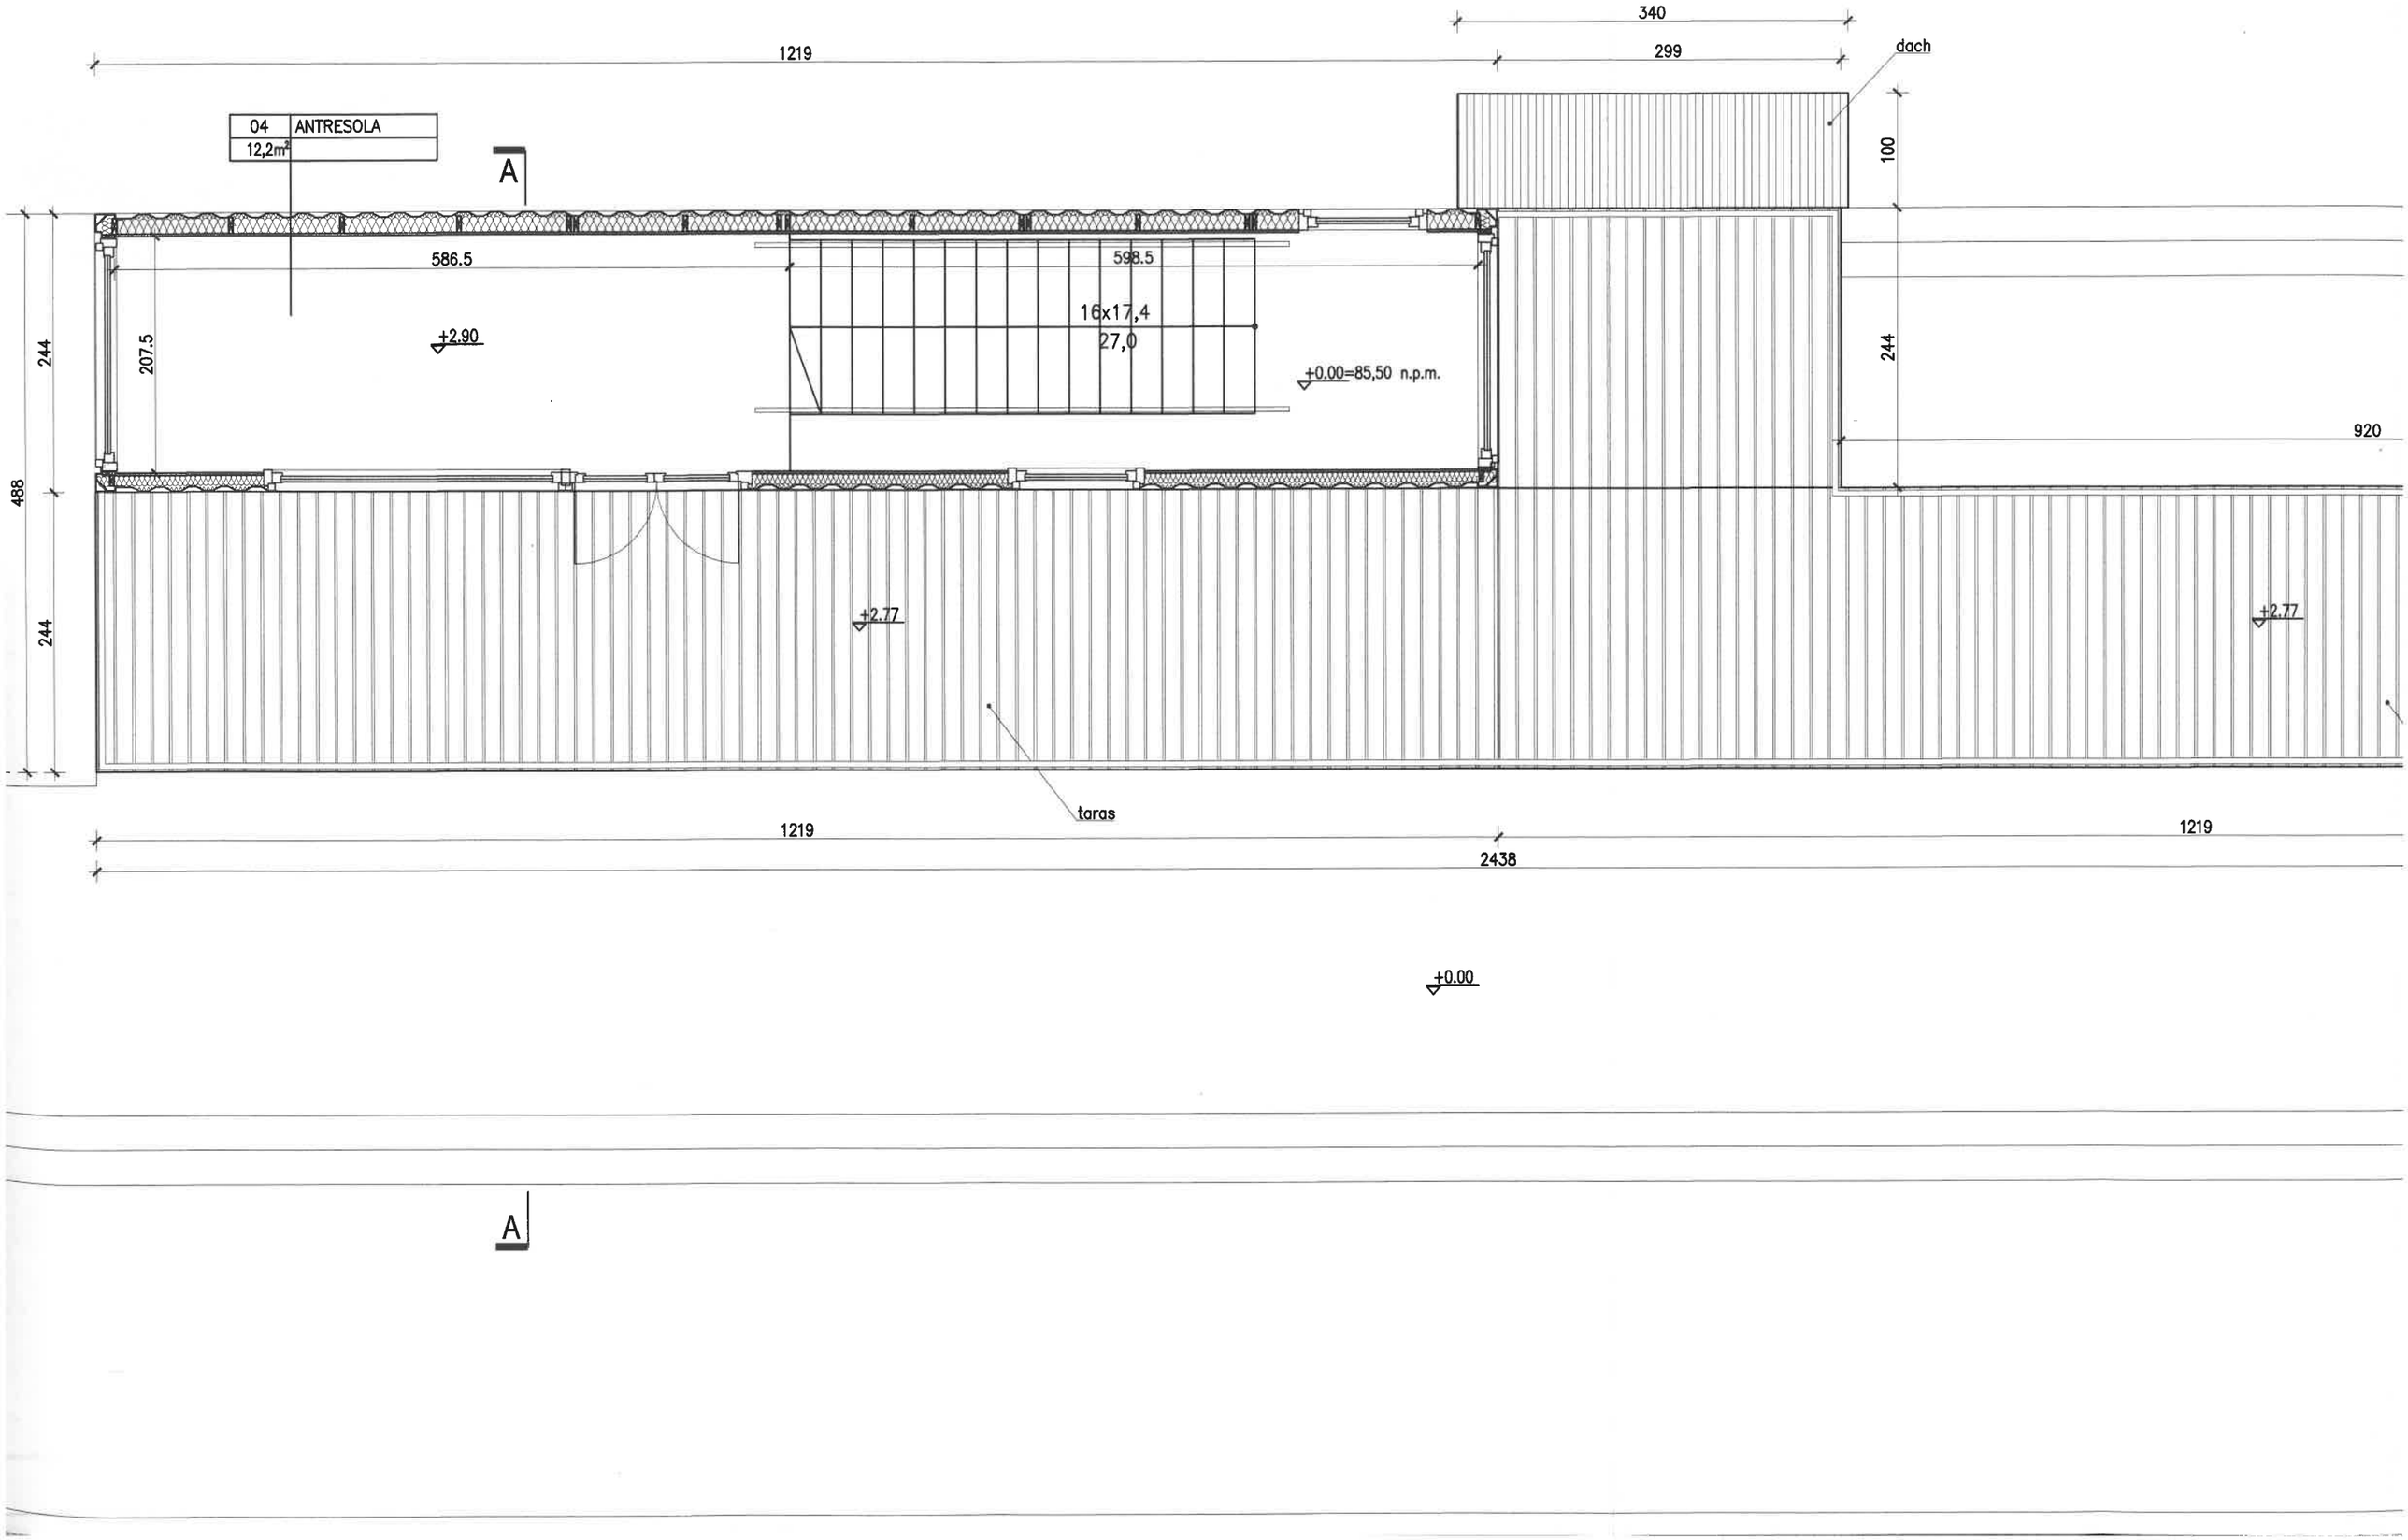

04 ANTRESOLA
12,2m²
A
1219
340
299
dach
100
586.5
598.5
16x17,4
27,0
+2.90
+0.00=85,50 n.p.m.
207.5
244
488
244
244
920
+2.77
+2.77
taras
1219
2438
1219
+0.00
A