
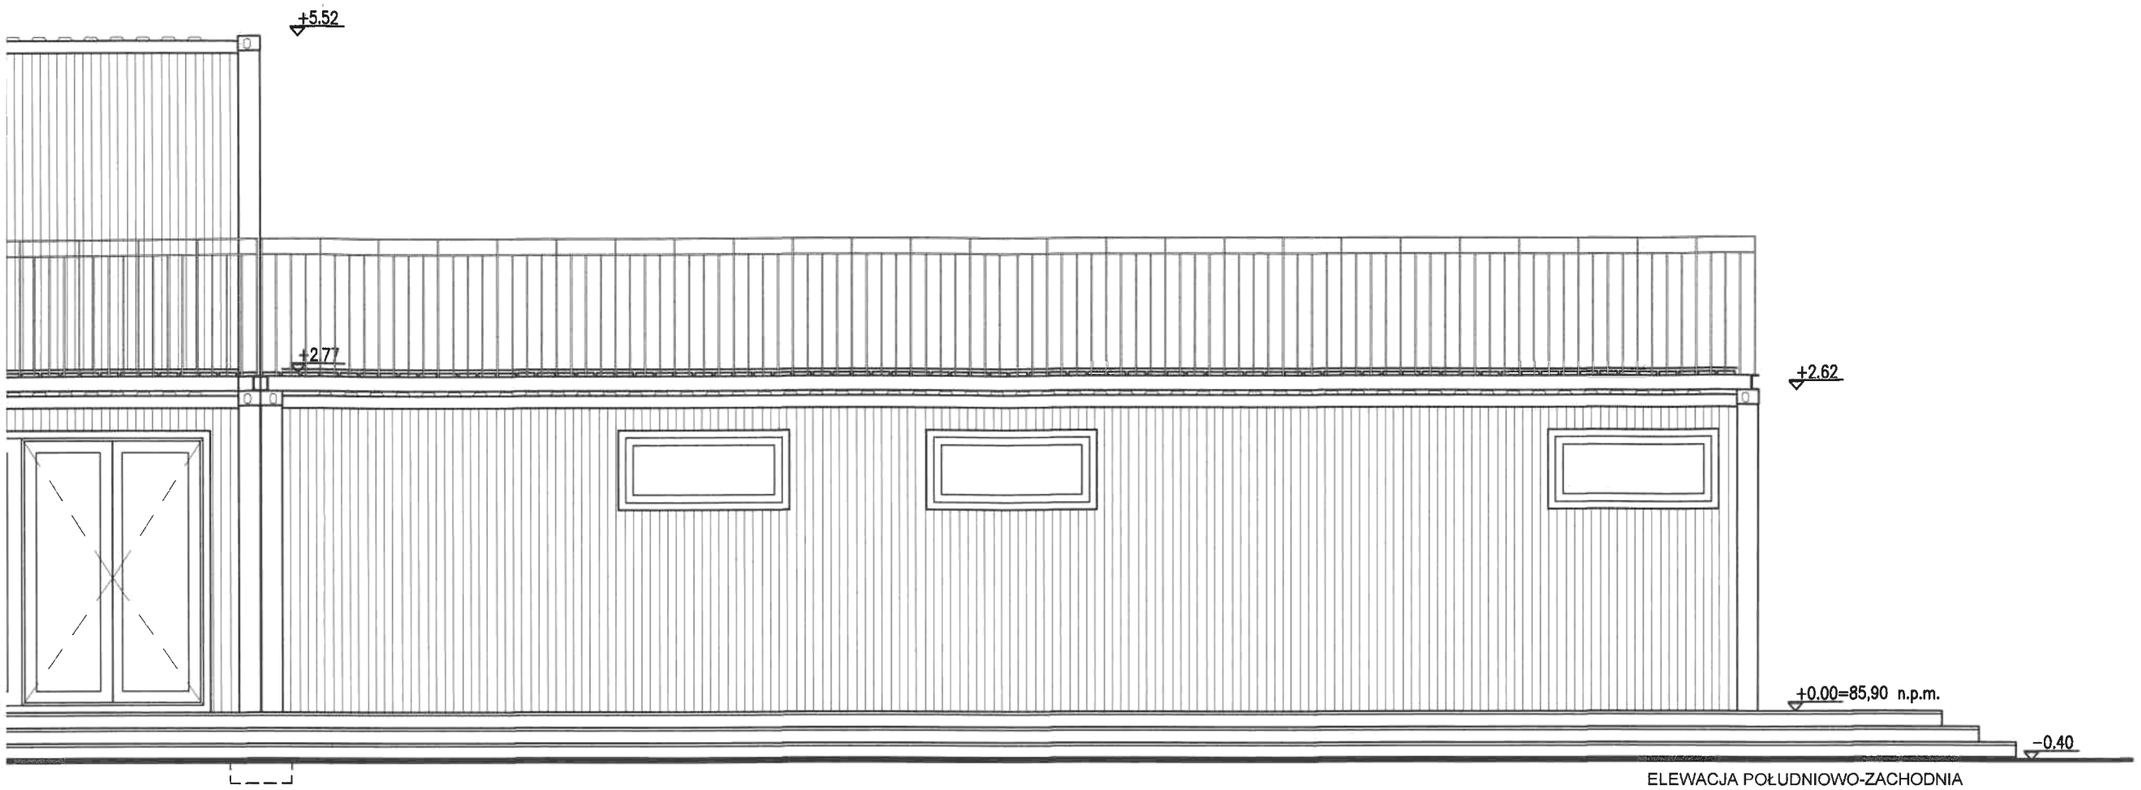


ELEWACJA POŁUDNIOWO-ZACHODNIA

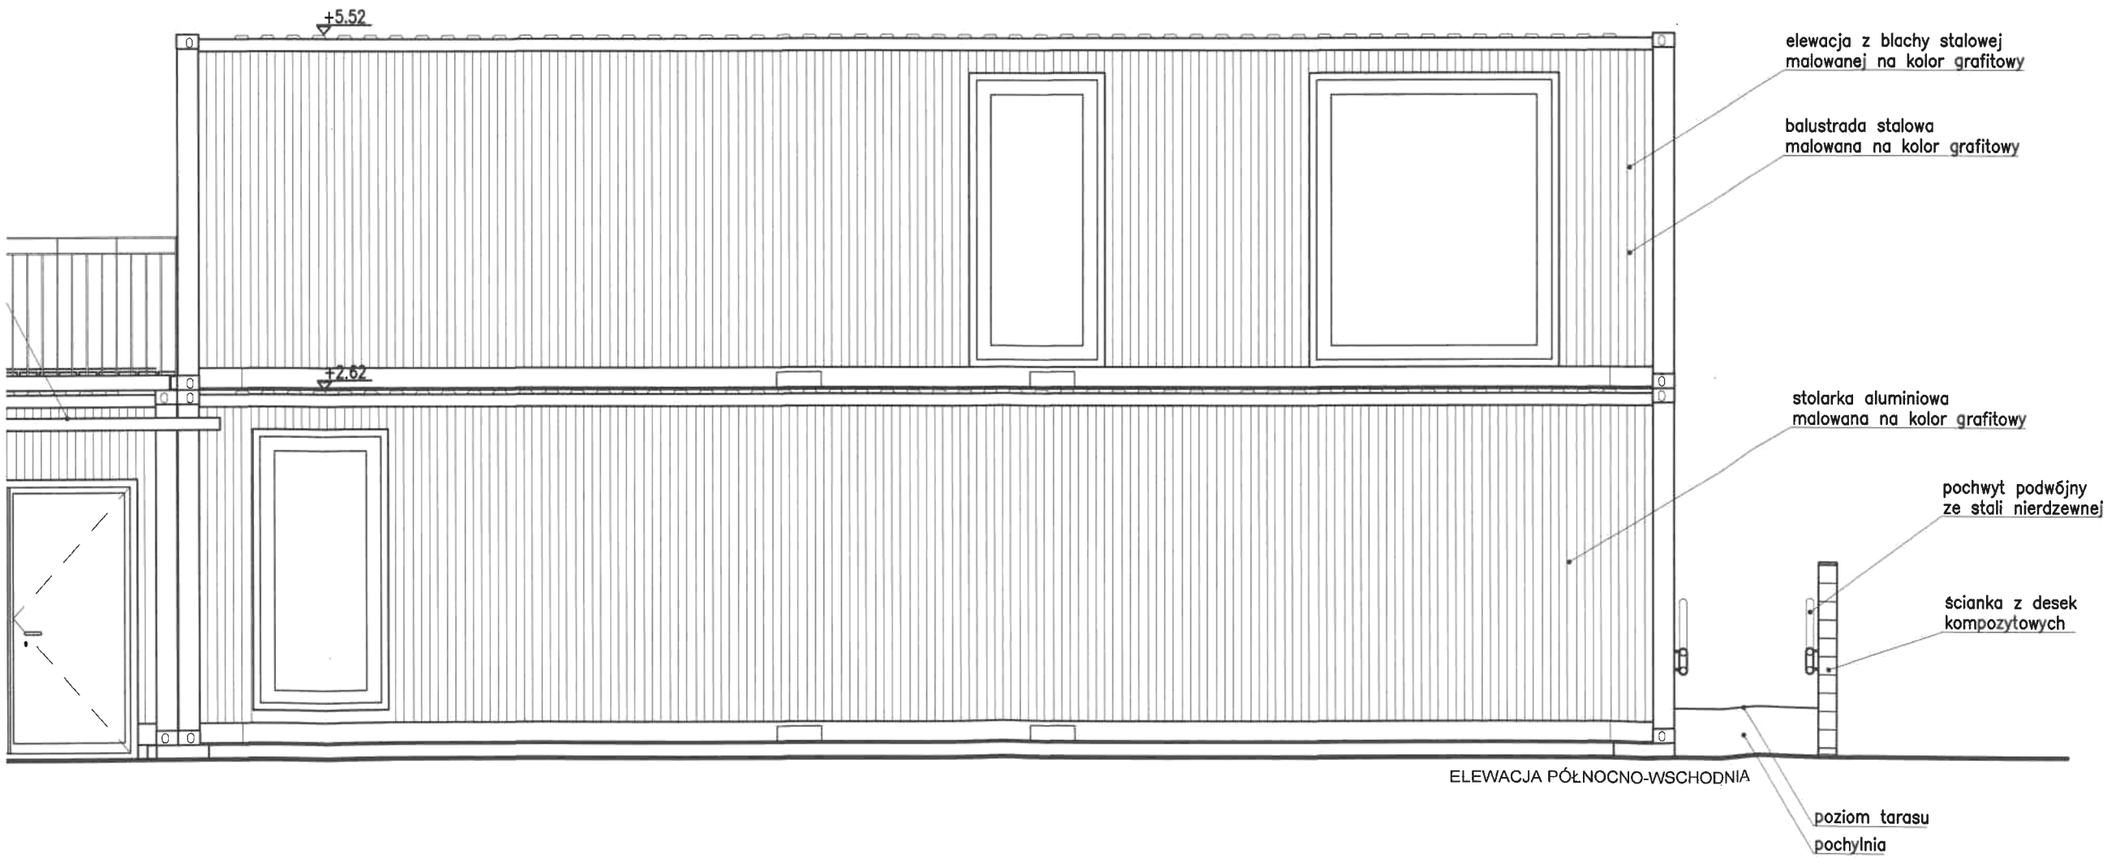

ELEWACJA PÓŁNOCNO-WSCHODNIA

BUDOWA KONTENEROWEGO
BUDYNKU USŁUGOWEGO
WRAZ Z ZAGOSPODAROWANIEM TERENU
ul. Terespolska, Warszawa
dz. ew.4/1, obręb 30208

ETAP:
PROJEKT ARCHITEKTONICZNO-BUDOWLANY

INWESTOR:
Miasto Stołeczne Warszawa
Dzielnica Praga–Południe
ul. Grochowska 274, 03-841 Warszawa

Woźnicki, Zdanowicz
ARCHITEKCI
02-555 Warszawa, Al. Niepodległości 157 lok.6

AUTORZY:
arch. Bartosz Zdanowic
nr upr.: MA 089/04

BUDYNEK
ELEWACJE DŁUGIE

branża: ARCHITEKTURA
data: 17.07.2026 skala: 1:50

A-03