

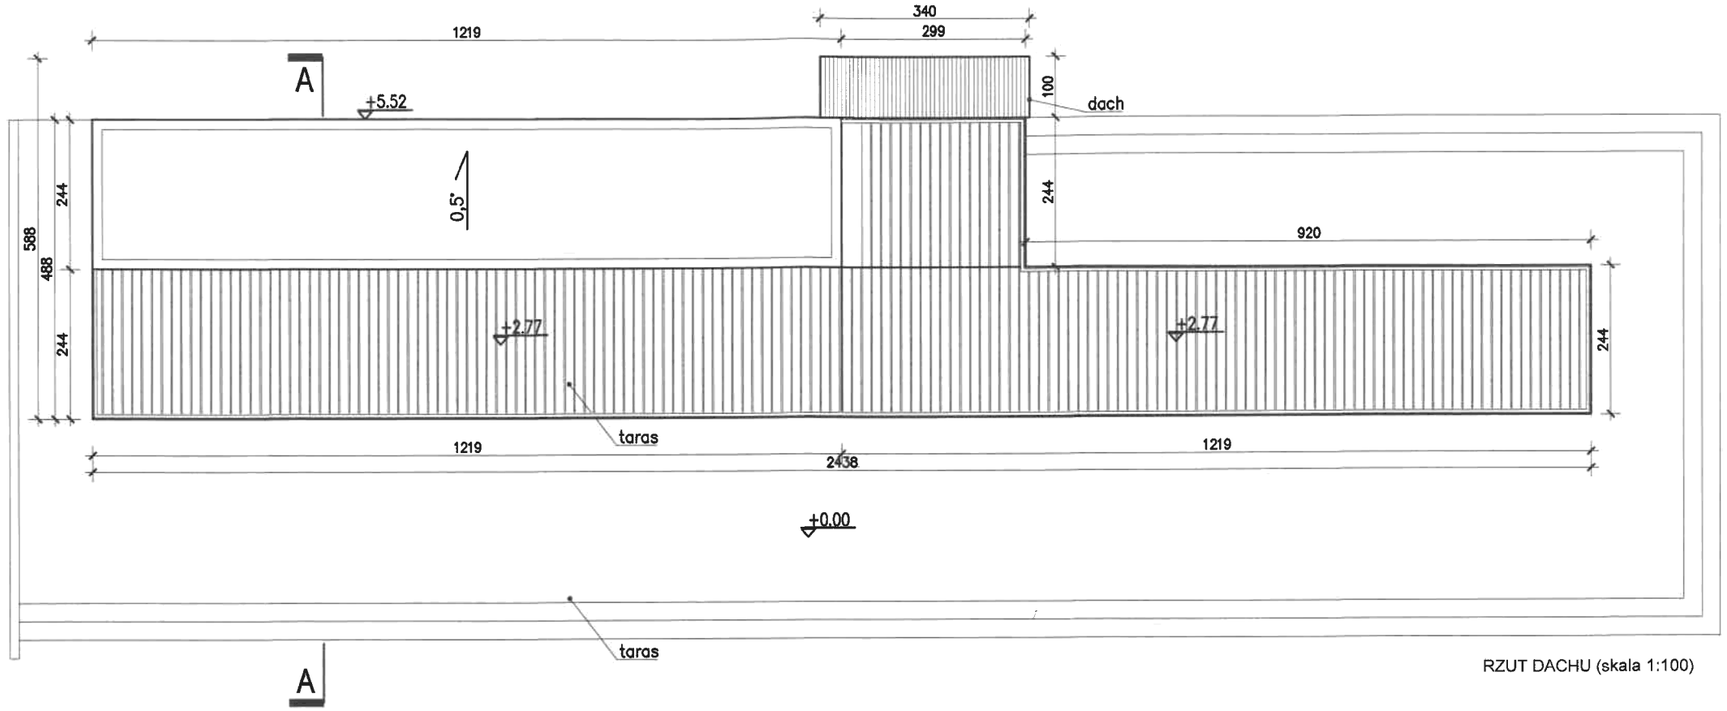



RZUT DACHU (skala 1:100)

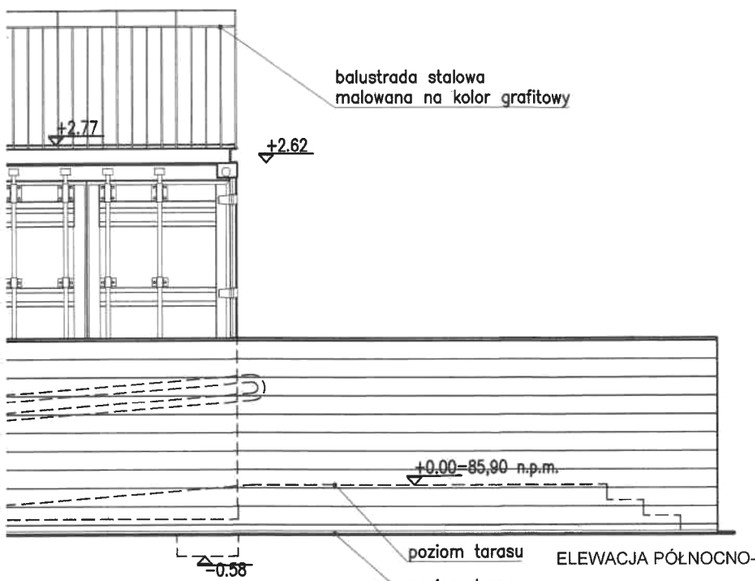

ELEWACJA PÓŁNOCNO-WSCHODNIA

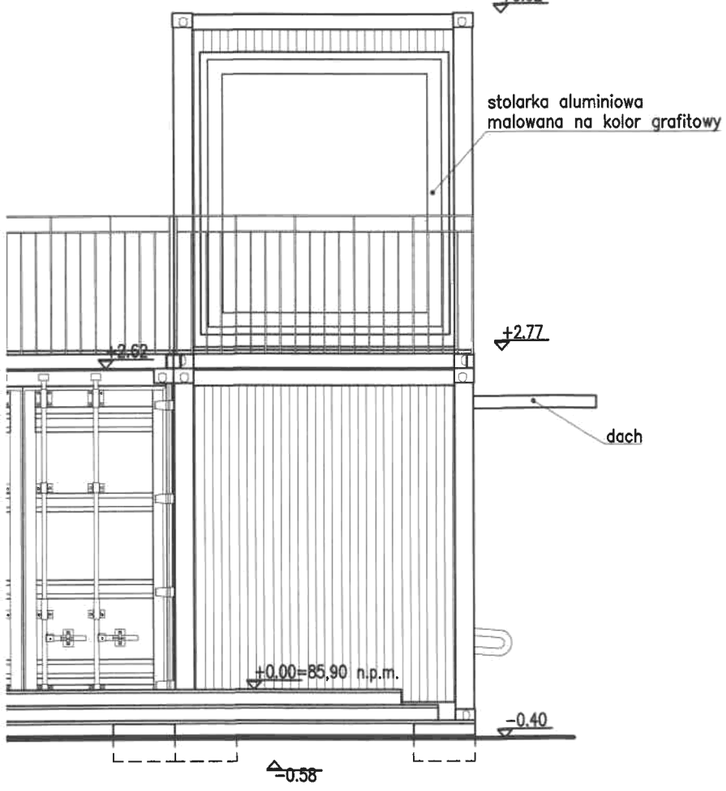

ELEWACJA POŁUDNIOWO-ZACHODNIA

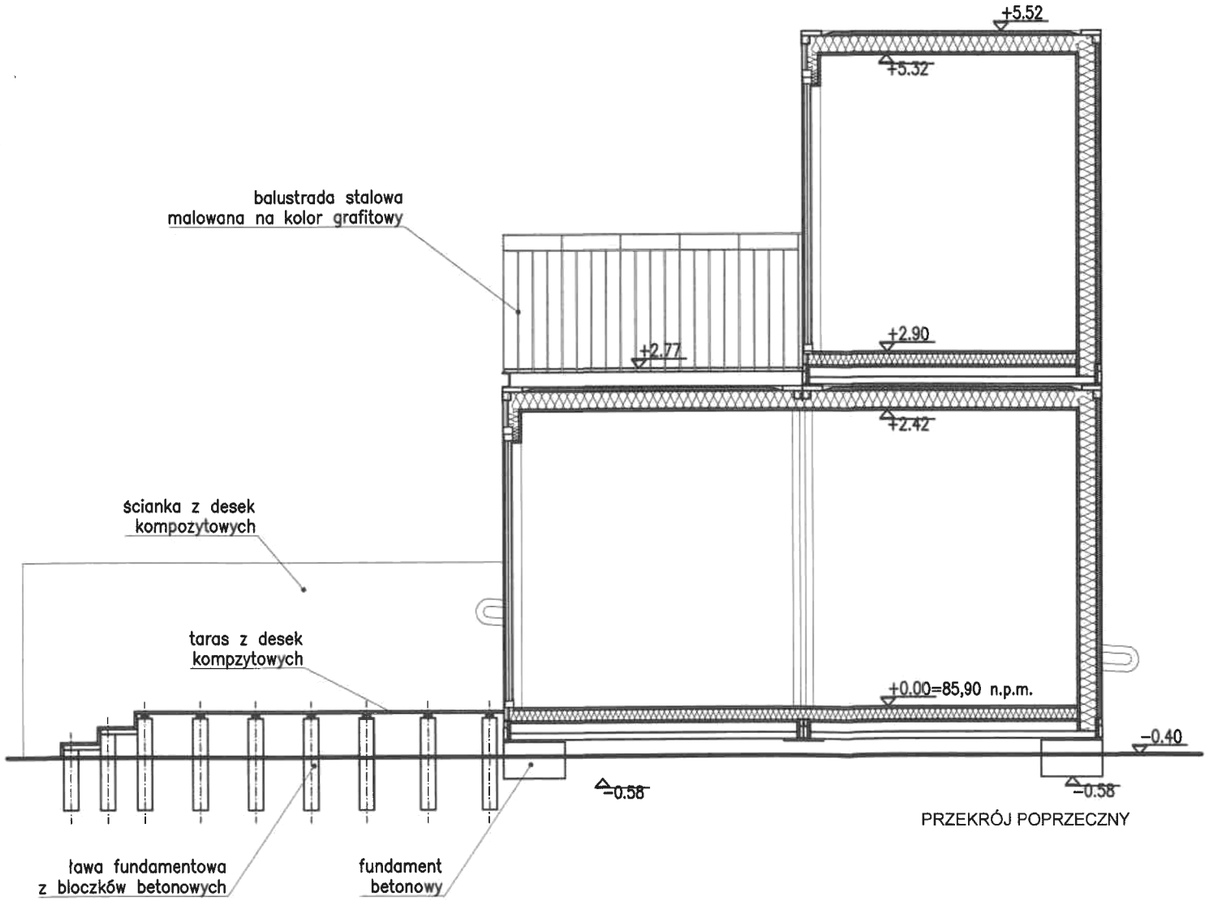

PRZEKRÓJ POPRZECZNY

BUDOWA KONTENEROWEGO
BUDYNKU USŁUGOWEGO
WRAZ Z ZAGOSPODAROWANIEM TERENU
ul. Terespolska, Warszawa
dz. ew.4/1, obręb 30208

ETAP:
PROJEKT ARCHITEKTONICZNO-BUDOWLANY

INWESTOR:
Miasto Stołeczne Warszawa
Dzielnica Praga–Południe
ul. Grochowska 274, 03-841 Warszawa

Woźnicki, Zdanowicz
ARCHITEKCI
02-555 Warszawa, Al. Niepodległości 157 lok.6

AUTORZY:
arch. Bartosz Zdanowicz
nr upr.: MA 089/04

BUDYNEK -RZUT DACHU,
ELEWACJE KRÓTKIE, PRZEKRÓJ

branża:	ARCHITEKTURA	A-04
data: 17.07.2026	skala: 1:100/1:50	