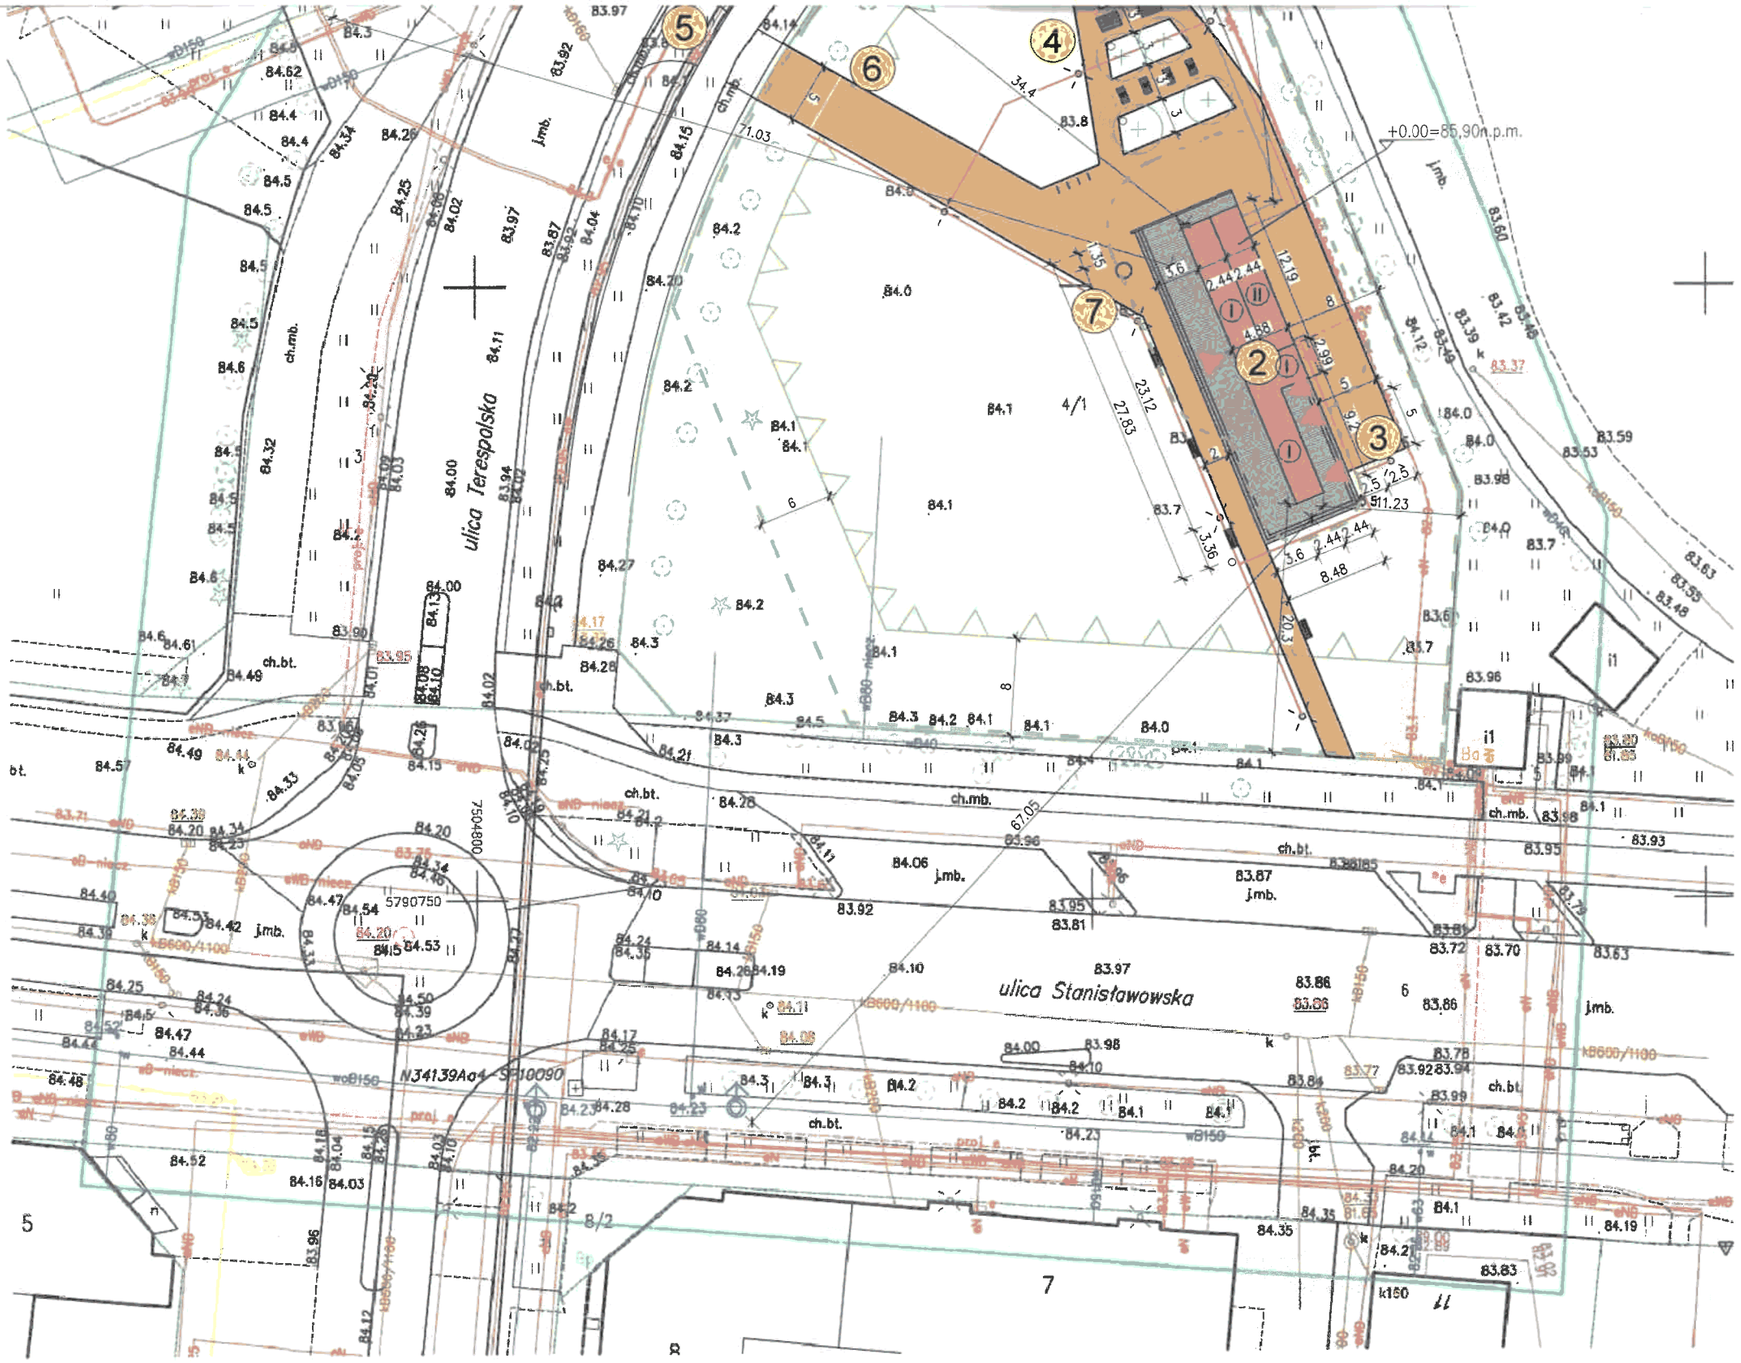


UTWARDZENIA MINERALNO-ŻYWICZNE projektowane

PROJEKTOWANA LATARNIA PARKOWA

KANALIZACJA SANITARNA

WODOCIĄG

KABLE ELEKTRYCZNE

ISTNIEJĄCY HYDRANT POŻAROWY

WEJŚCIA DO BUDYNKU

STÓŁ SZACHOWY

STÓŁ Z ŁAWAMI

ŁAWKA

KOSZ NA ODPADKI

STOJAK DLA ROWERÓW

ZA ZGODNOŚĆ Z ORYGINAŁEM

mgr inż. [illegible]owicz
uprawn[illegible]wania
bez ograni[illegible]tonicznej
nr ew. uprawnień MA/089/04

MAPA DO CELÓW PROJEKTOWYCH

dla terenu położonego przy ul. Terespolskiej w Warszawie

Oznaczenie kancelaryjne pracy geodezyjnej		BG-WOZ-OZ.6640.5545.2026.PGE
Jednostka ewidencyjna	identyfikator	146507_8
	nazwa	Dzielnica Praga-Południe
Obręb ewidencyjny	identyfikator	146507_8.0208
	nazwa	3-02-08
Skala/sekcja mapy	1:500	numeryczna
Nazwa układu współrzędnych	prostokątnych płaskich	PUWG 2000
	wysokościowych	PL-EVRF2007_NH
Oznaczenie granic obszaru, który był przedmiotem aktualizacji		Kolorem błękitnym

Oznaczenie i informacje o służebnościach gruntowych mających wpływ na zagospodarowanie gruntów zlokalizowanych w granicach projektowanej inwestycji	Wykonano bez ustalenia obciążeń
Oznaczenie i symbol konturu użytku gruntowego, który nie jest ujawniony w bazie danych ewidencji gruntów i budynków	Brak
Nie wyklucza się istnienia w terenie innych, nie wykazanych na niniejszej mapie urządzeń podziemnych, które nie były zgłoszone do inwentaryzacji.	

GEO-ASTRA
WITOLD PASZKOWSKI
ul. Bitwy Warszawskiej 1920r. 21/156
02-366 Warszawa NIP 7272409184
tel. 531 600 531 tel./ fax 22 659 69 76
geo-astra@wp.pl REGON 145566893
nazwa wykonawcy

15.07.2026
mgr [illegible]ki
numer uprawnień 20266
data i podpis geodety uprawnionego

Poświadczam, że niniejszy dokument został opracowany w wyniku prac geodezyjnych i kartograficznych, których rezultaty zawiera operat techniczny pozytywnie zweryfikowany. Jednocześnie informuję, że jestem świadomy odpowiedzialności karnej za złożenie fałszywego oświadczenia.

Identyfikator zgłoszenia prac geodezyjnych	BG-WOZ-OZ.6640.5545.2026.PGE
Organ służby geodezyjnej, który otrzymał zgłoszenie	Prezydent M St. Warszawy
Wykonawca prac geodezyjnych	GEO-ASTRA Witold Paszkowski
Nr i data sporządzenia dokumentu zawierającego wynik pozytywnej weryfikacji	Protokół Weryfikacji nr BG-WOZ-OZ.6640.5545.2026.PGE_163389 z dnia 15.07.2026
Imię i nazwisko oraz numer uprawnień zawodowych kierownika prac	Witold Paszkowski Nr uprawnień 20266

Ge[illegible]
mgr i[illegible]
numer uprawnień 20266

BUDOWA KONTENEROWEGO BUDYNKU USŁUGOWEGO WRAZ Z ZAGOSPODAROWANIEM TERENU
ul. Terespolska, Warszawa
dz. ew.4/1, obręb 30208

ETAP:
PROJEKT ZAGOSPODAROWANIA TERENU

INWESTOR:
Miasto Stołeczne Warszawa
Dzielnica Praga–Południe
ul. Grochowska 274, 03-841 Warszawa

Woźnicki, Zdanowicz
ARCHITEKCI
02-555 Warszawa, Al. Niepodległości 157 lok.6

AUTORZY:	branża:	ARCHITEK[illegible]
Projekt.:	arch. Bartosz Zdanowicz	nr upr.: MA 089/04
	branża:	SANITAR[illegible]
Projekt.:	mgr inż. Maria Ignaczewsk[illegible]	nr upr. St-121/86
	branża:	ELEKTRYCZNA
Projekt.:	mgr inż.Daniel Dobrowolski	MAZ/0202/PBE/18

PROJEKT ZAGOSPODAROWANIA TERENU

data: 05.08.2026 skala: 1:500 Z-01